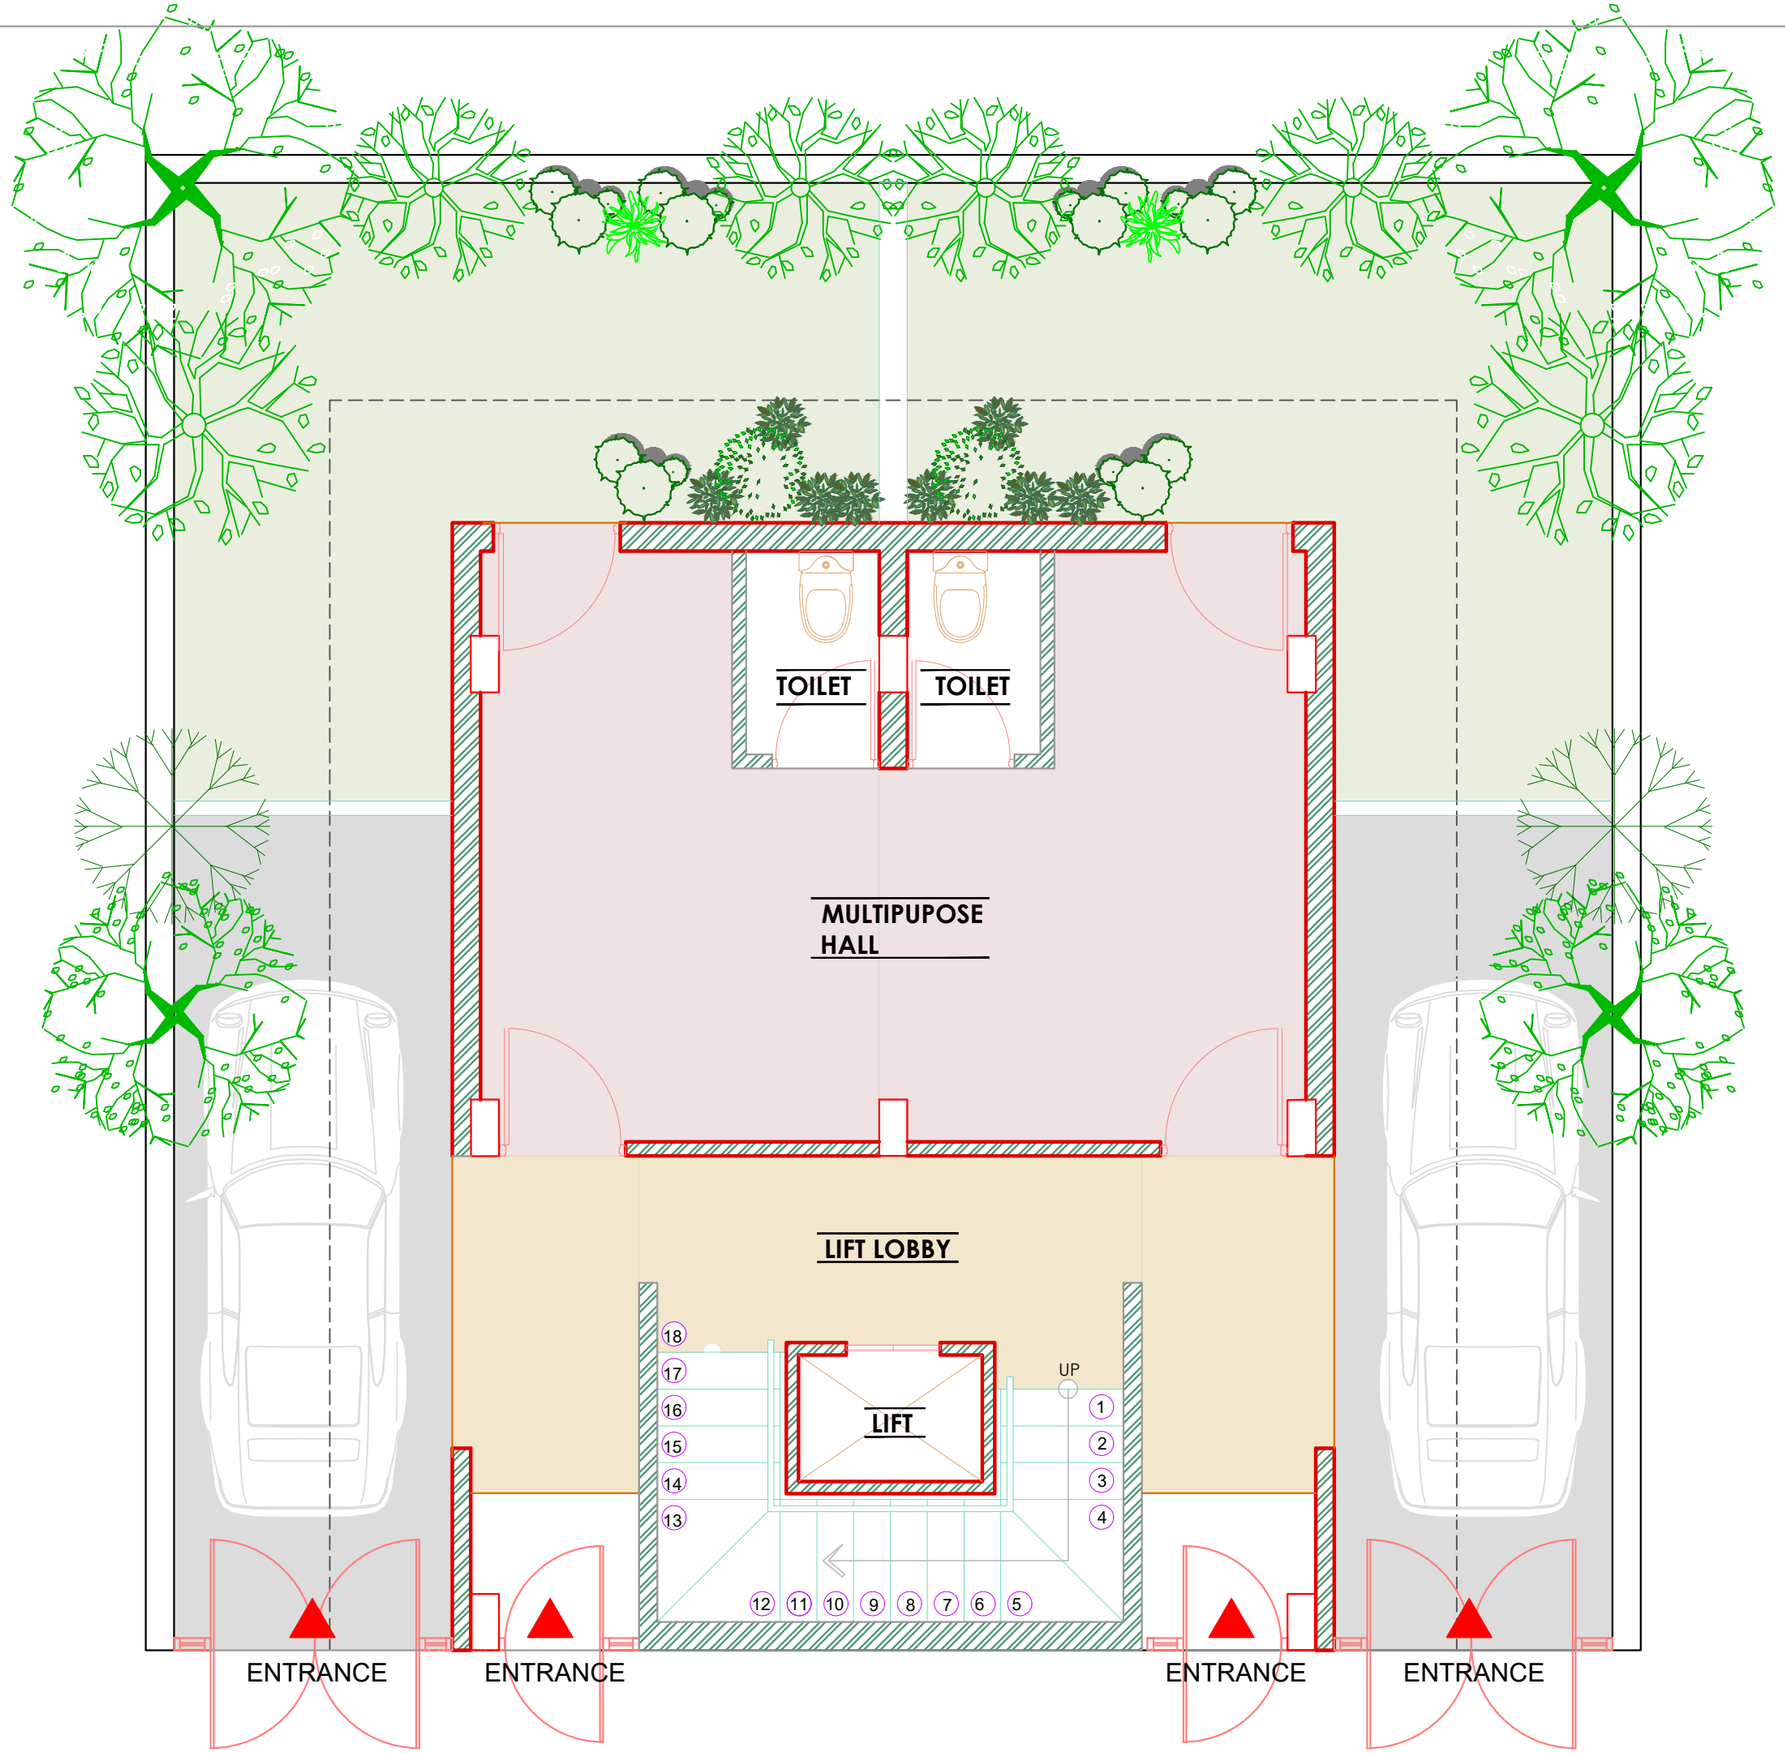

PROJECT NAME

BUNGLOW

BARODA

DATE : 16th MARCH' 25

SCALE

1:50

DRAWING TITLE

GROUND FLOOR PLAN

FOR REFERNCE

DRAFT BY:

KUSHAL SHAH

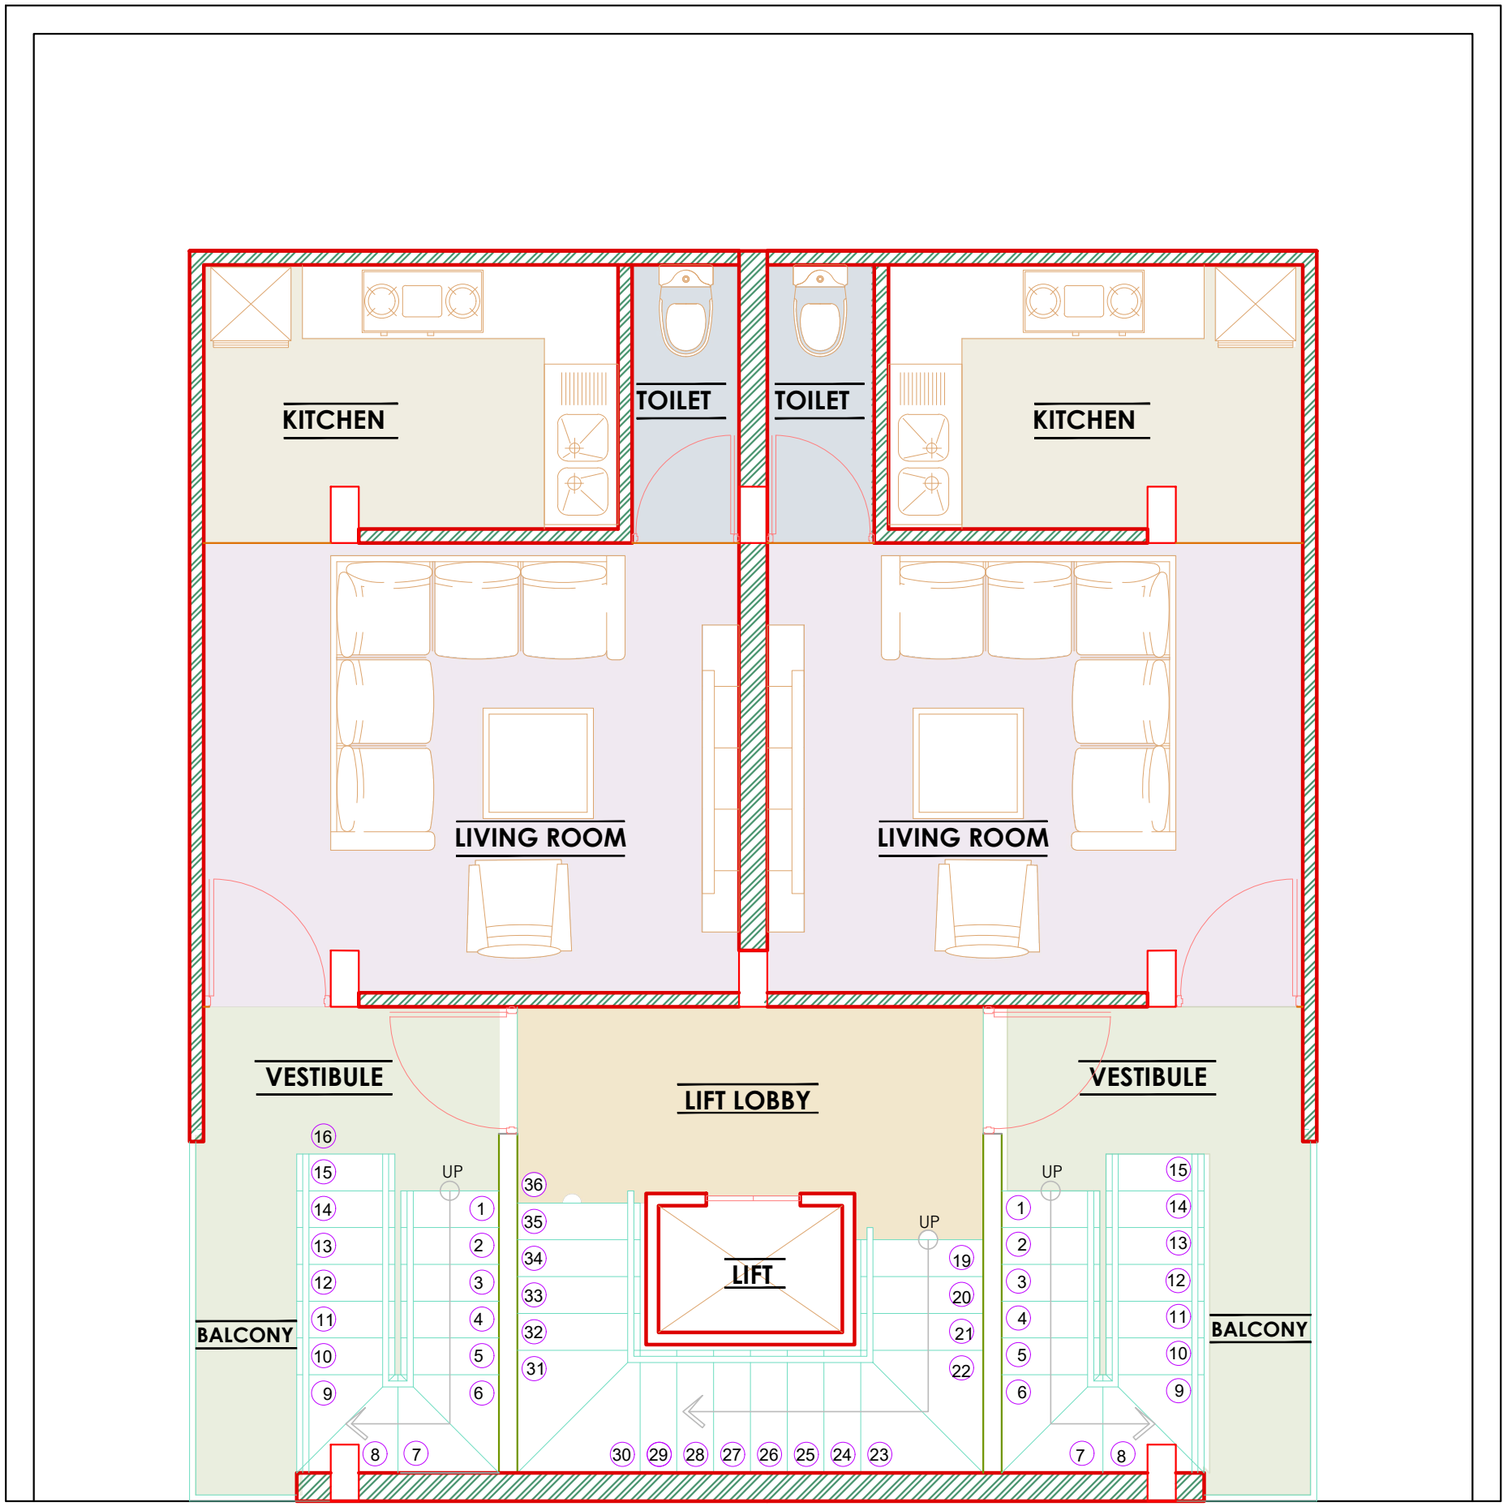

PROJECT NAME

BUNGLOW

BARODA

DATE : 16th MARCH' 25

SCALE

1:50

DRAWING TITLE

FIRST FLOOR PLAN

FOR REFERNCE

DRAFT BY:

KUSHAL SHAH

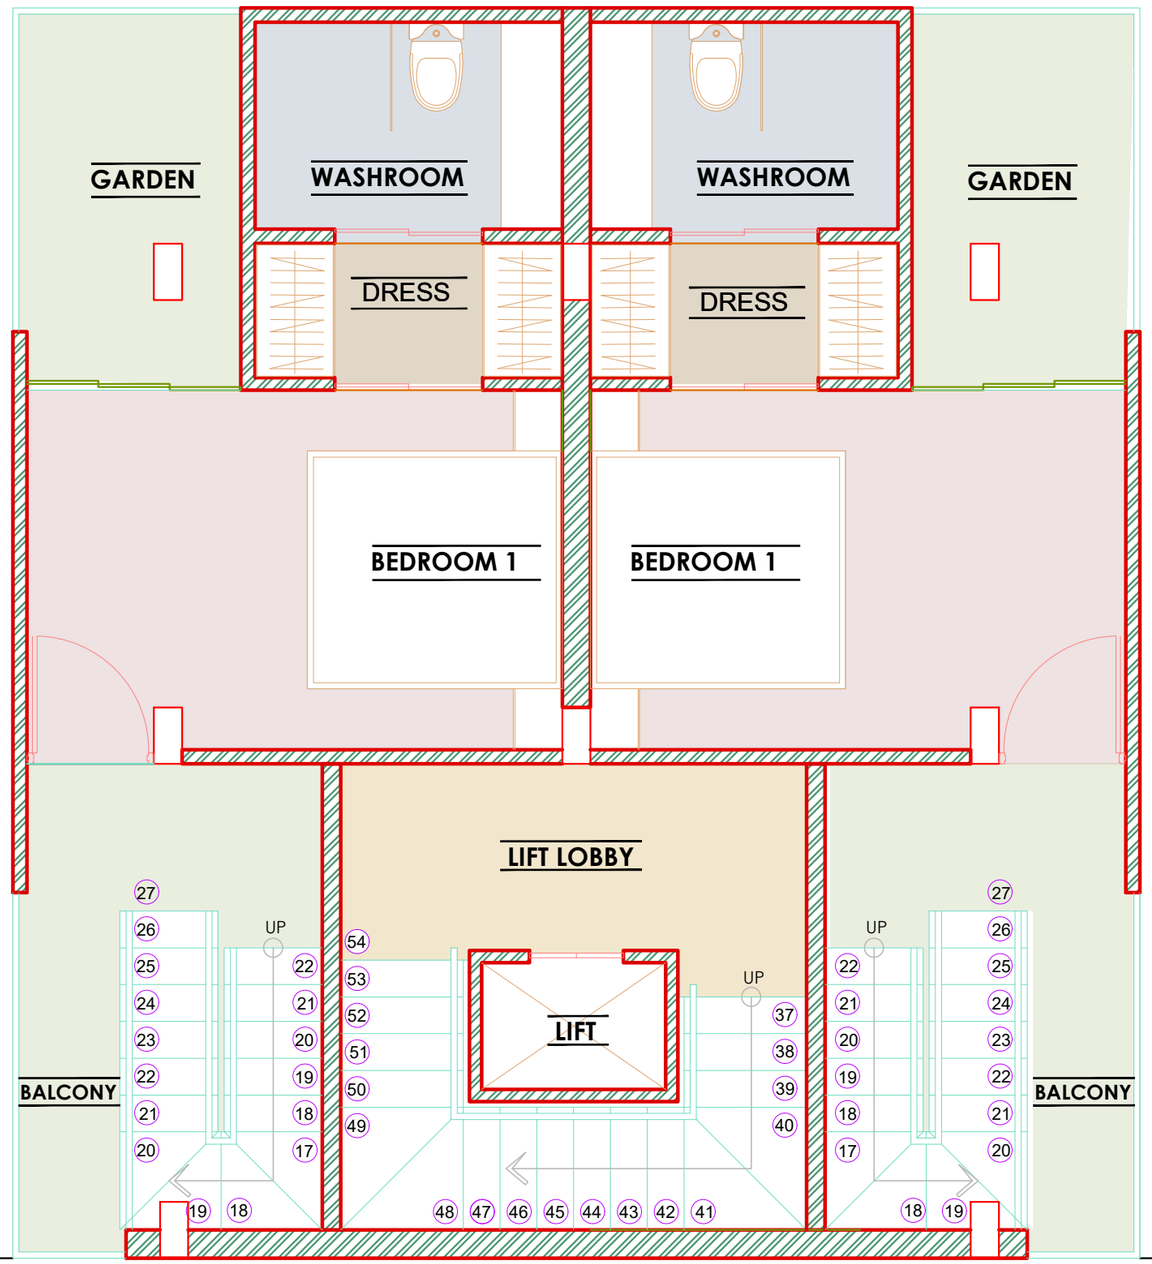

PROJECT NAME

BUNGLOW

BARODA

DATE : 16th MARCH' 25

SCALE

1:50

DRAWING TITLE

SECOND FLOOR PLAN

FOR REFERNCE

DRAFT BY:

KUSHAL SHAH

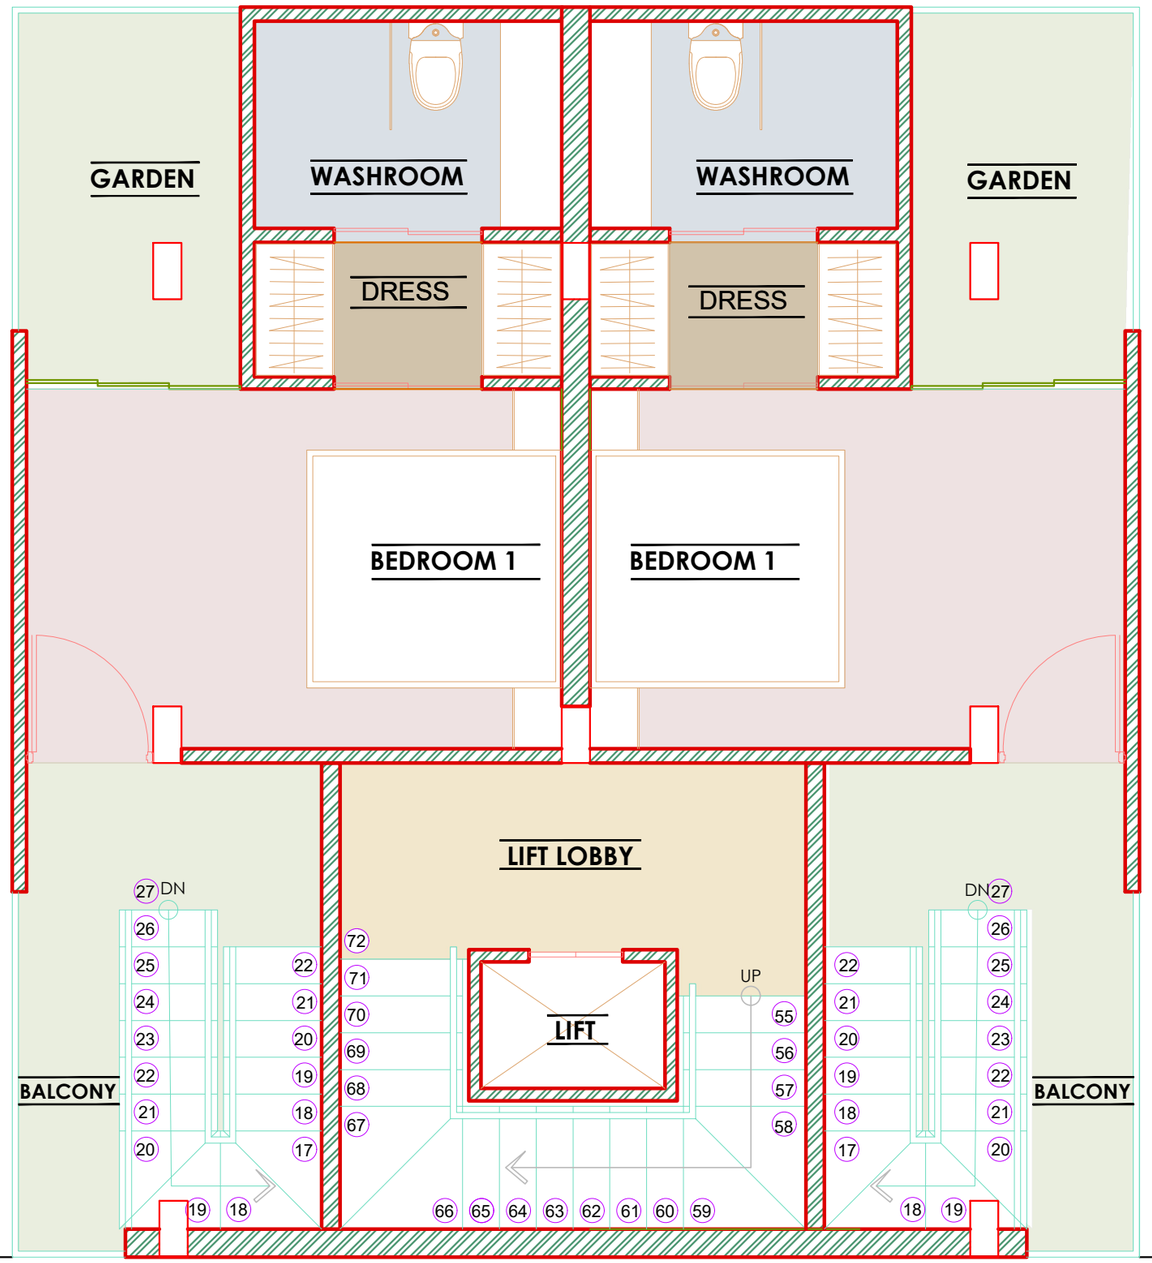

PROJECT NAME

BUNGLOW

BARODA

DATE : 16th MARCH' 25

SCALE

1:50

DRAWING TITLE

THIRD FLOOR PLAN

FOR REFERNCE

DRAFT BY:

KUSHAL SHAH

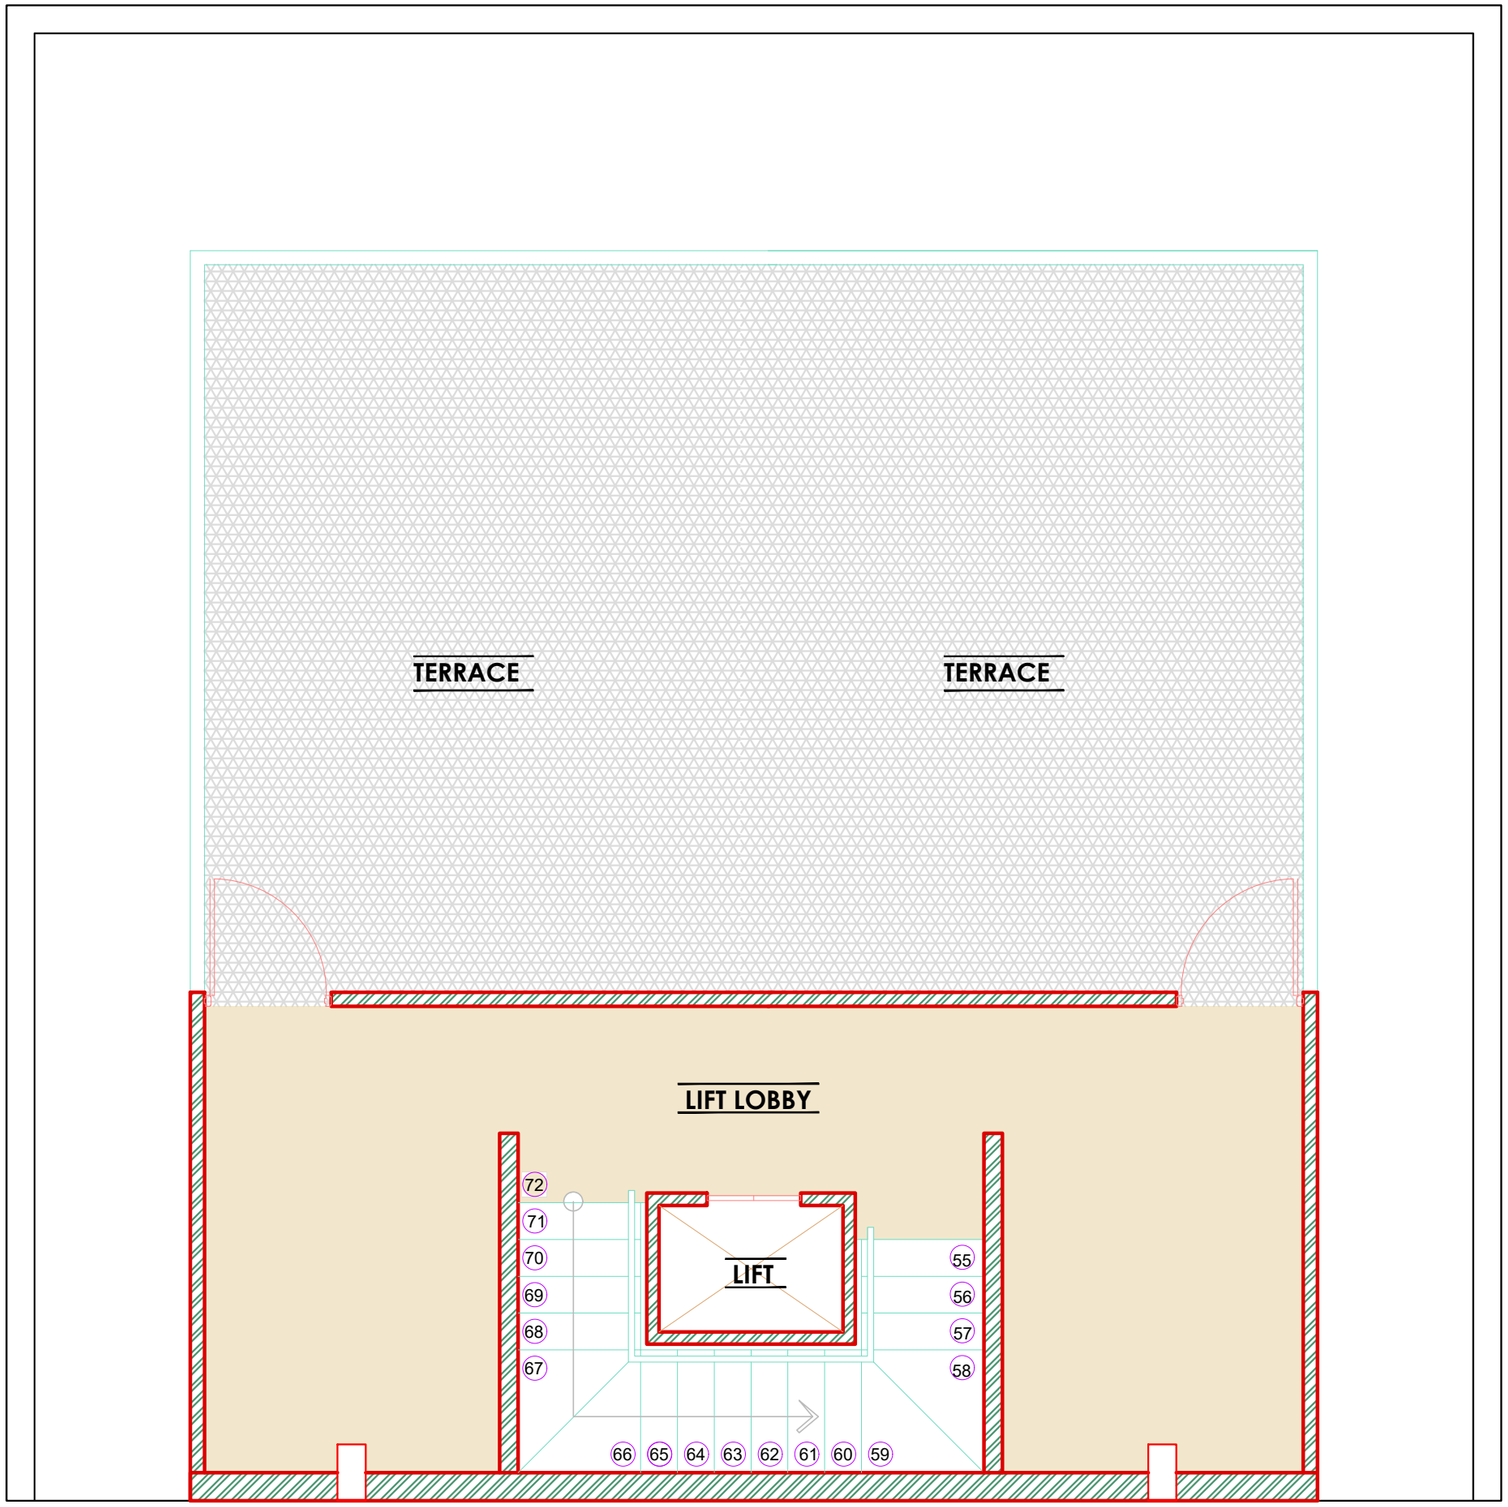

PROJECT NAME

BUNGLOW

BARODA

DATE : 16th MARCH' 25

SCALE

1:50

DRAWING TITLE

TERRACE FLOOR PLAN

FOR REFERNCE

DRAFT BY:

KUSHAL SHAH